

ДОМАШНЯ МАЙСТЕРНЯ 5000 × 2800

Каркасна холодна майстерня для обслуговування будинку · Київ · ескізний проєкт

Відомість аркушів

1	Загальні дані, позначення, примітки
2	План фундаменту. Переріз стрічки
3	План на відм. ±0.000. Розстановка
4	Фасади: південний, північний, східний, західний
5	Розрізи А–А, Б–Б
6	Розрізи В–В, Г–Г (розгортки стін)
7	Робоча поверхня і шафи
8	Каркас: стіни та дах
9	Вузли 1–3: цоколь, карниз, задній карниз
10	Вузли 4–6: кут, поріг, шари стіни
11	Специфікація матеріалів

Основні показники

Габарити зовні	5000 × 2800 мм
Габарити всередині	4736 × 2536 мм
Площа забудови	14,0 м²
Корисна площа підлоги	12,0 м²
Висота стін	3000 мм (фасад) / 2500 мм (зад) від підлоги
Дах	односхилий, нахил 10,1° (≈ 1 : 5,6), бітумна черепиця по OSB 18
Фундамент	стрічка 200 × 500 мм, цоколь +200 мм
Каркас	брус 100 × 100, крок стійок ≈ 600 мм
Двері	алюмінієві скляні 900 × 2200, південь
Вікон немає	світло: скляні двері + LED 4000 K
Підлога	бруківка 200 × 100 × 60

Умовні позначення

	Бетон стрічки (C16/20)
	Щебінь, подушка
	Пісок
	Ґрунт
	Бруківка 200×100×60
	Деревина (брус, дошка)
	OSB-3 (12 мм стіни, 18 мм дах)
	Бітумна черепиця
	Скло дверей

Примітки

- Усі розміри в міліметрах, позначки рівнів у метрах від ±0.000 (чиста підлога).
- ±0.000 = +0.200 над рівнем землі. Рівень землі позначено −0.200.
- Креслення ескізні, вони підлягають уточненню за результатами шурфа.
- Глибина стрічки 500 мм прийнята для неслучистого ґрунту. Нормативна глибина промерзання в Києві ≈ 0,9 м. При глині чи високих ґрунтових водах заглибити до 900 мм і додати дренаж.
- Перерізи кроквей 50×150 (крок ≈ 544 мм) перевірити за снігом для Києва.
- Колеса R21 на кронштейнах: розрахункове навантаження ≥ 100 кг на стопку.
- Бітумна черепиця: нахил 10° нижче рекомендованого (≥ 12° для звичайної черепиці). Обов'язковий підкладковий килим по всій площі, ґонт приклеювати на мастику, звіряти з інструкцією виробника.
- Утеплення відсутнє. Зберігати вентиляційні зазори і решітки.

Проєкт

Майстерня 5000 × 2800, Київ

Назва аркуша

Загальні дані

Ескізний проєкт · Дата 10.2026 · ±0.000 = рівень чистої підлоги



Масштаб

—

Аркуш

1 / 11

Переріз 1–1 (стрічка)

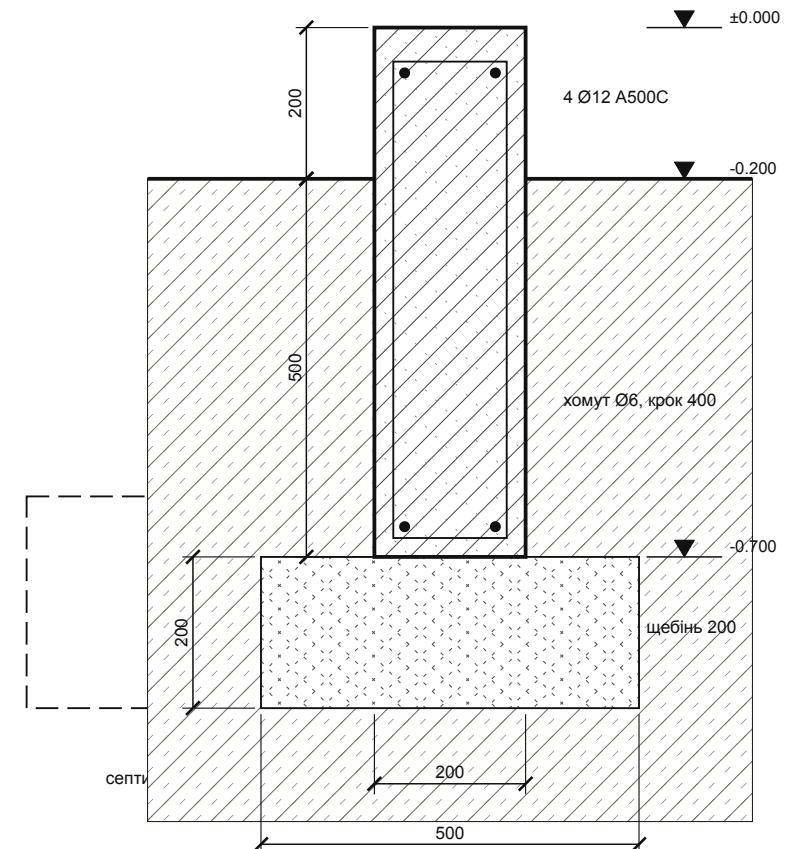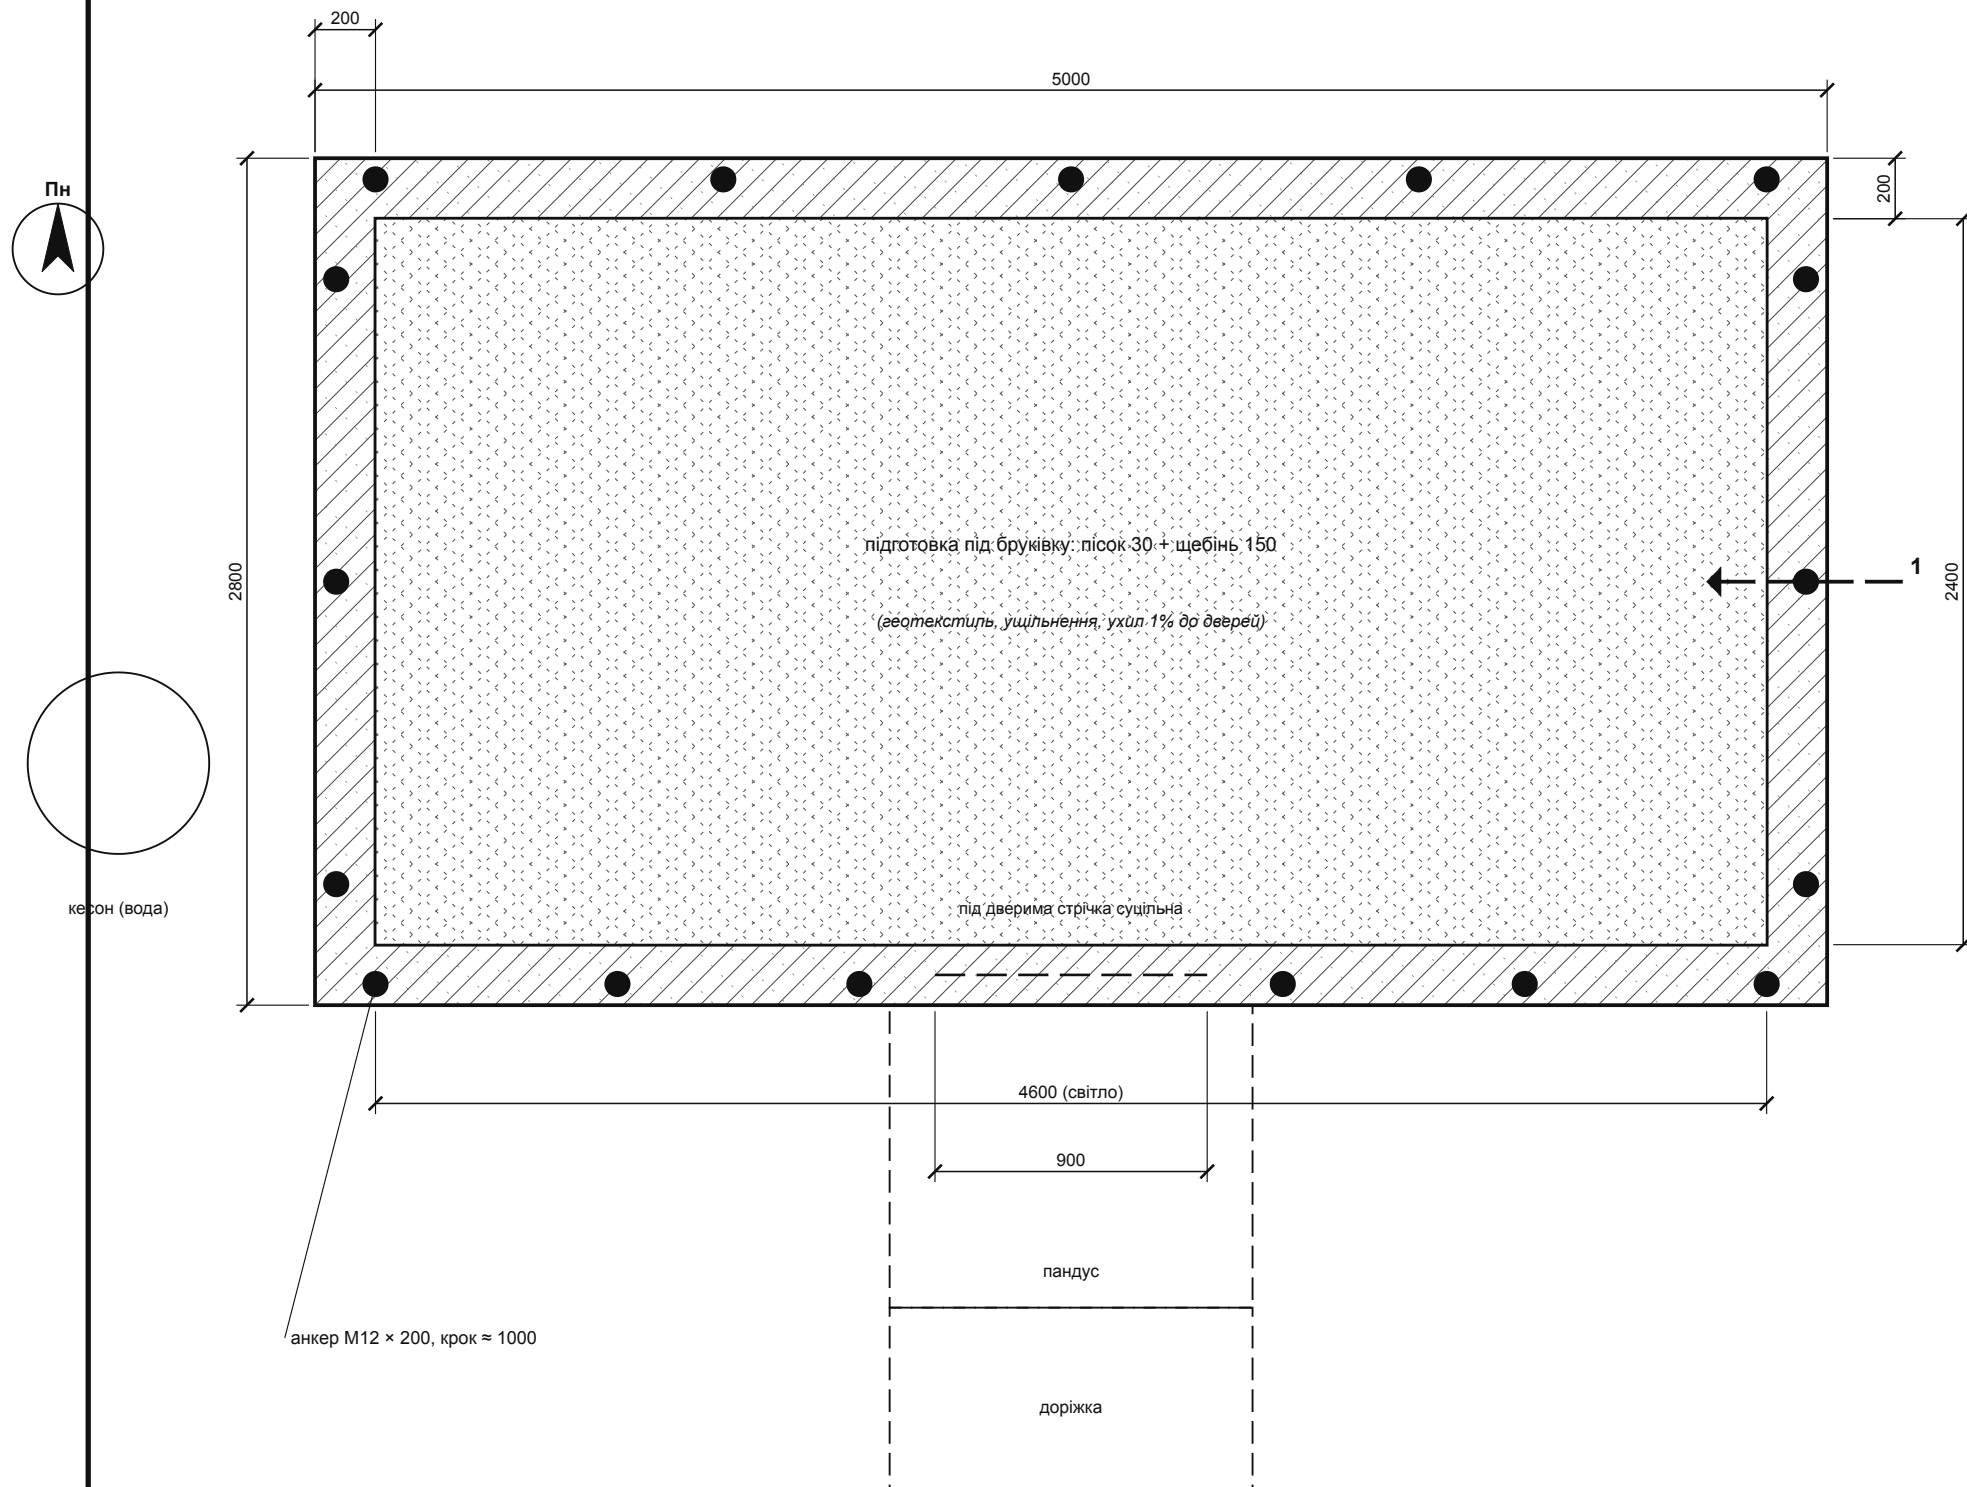

Бетон С16/20 (В15), F100. Опалубка над землею 200 мм.
Захисний шар арматури 30 мм. Гідроізоляція по верху
стрічки: 2 шари руберойду на бітумній мастиці.

Бетон стрічки: $\approx 2,1 \text{ м}^3$ ($14,8 \text{ м} \times 0,2 \times 0,7$). Арматура: $\approx 60 \text{ м } \varnothing 12 + \approx 55 \text{ м хомутів } \varnothing 6$.
Перед заливкою зняти родючий шар, ущільнити дно траншеї, відсипати щебінь 200 мм.

Проект

Майстерня 5000 × 2800, Київ

Назва аркуша

План фундаменту. Переріз стрічки



Ескізний проєкт · Дата 10.2026 · ±0.000 = рівень чистої підлоги

Масштаб

1:25 · 1:10

Аркуш

2 / 11

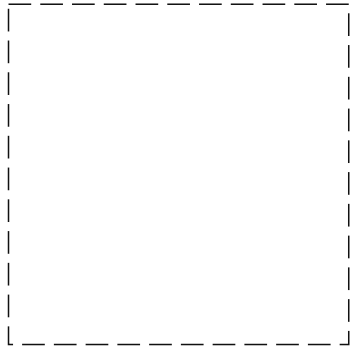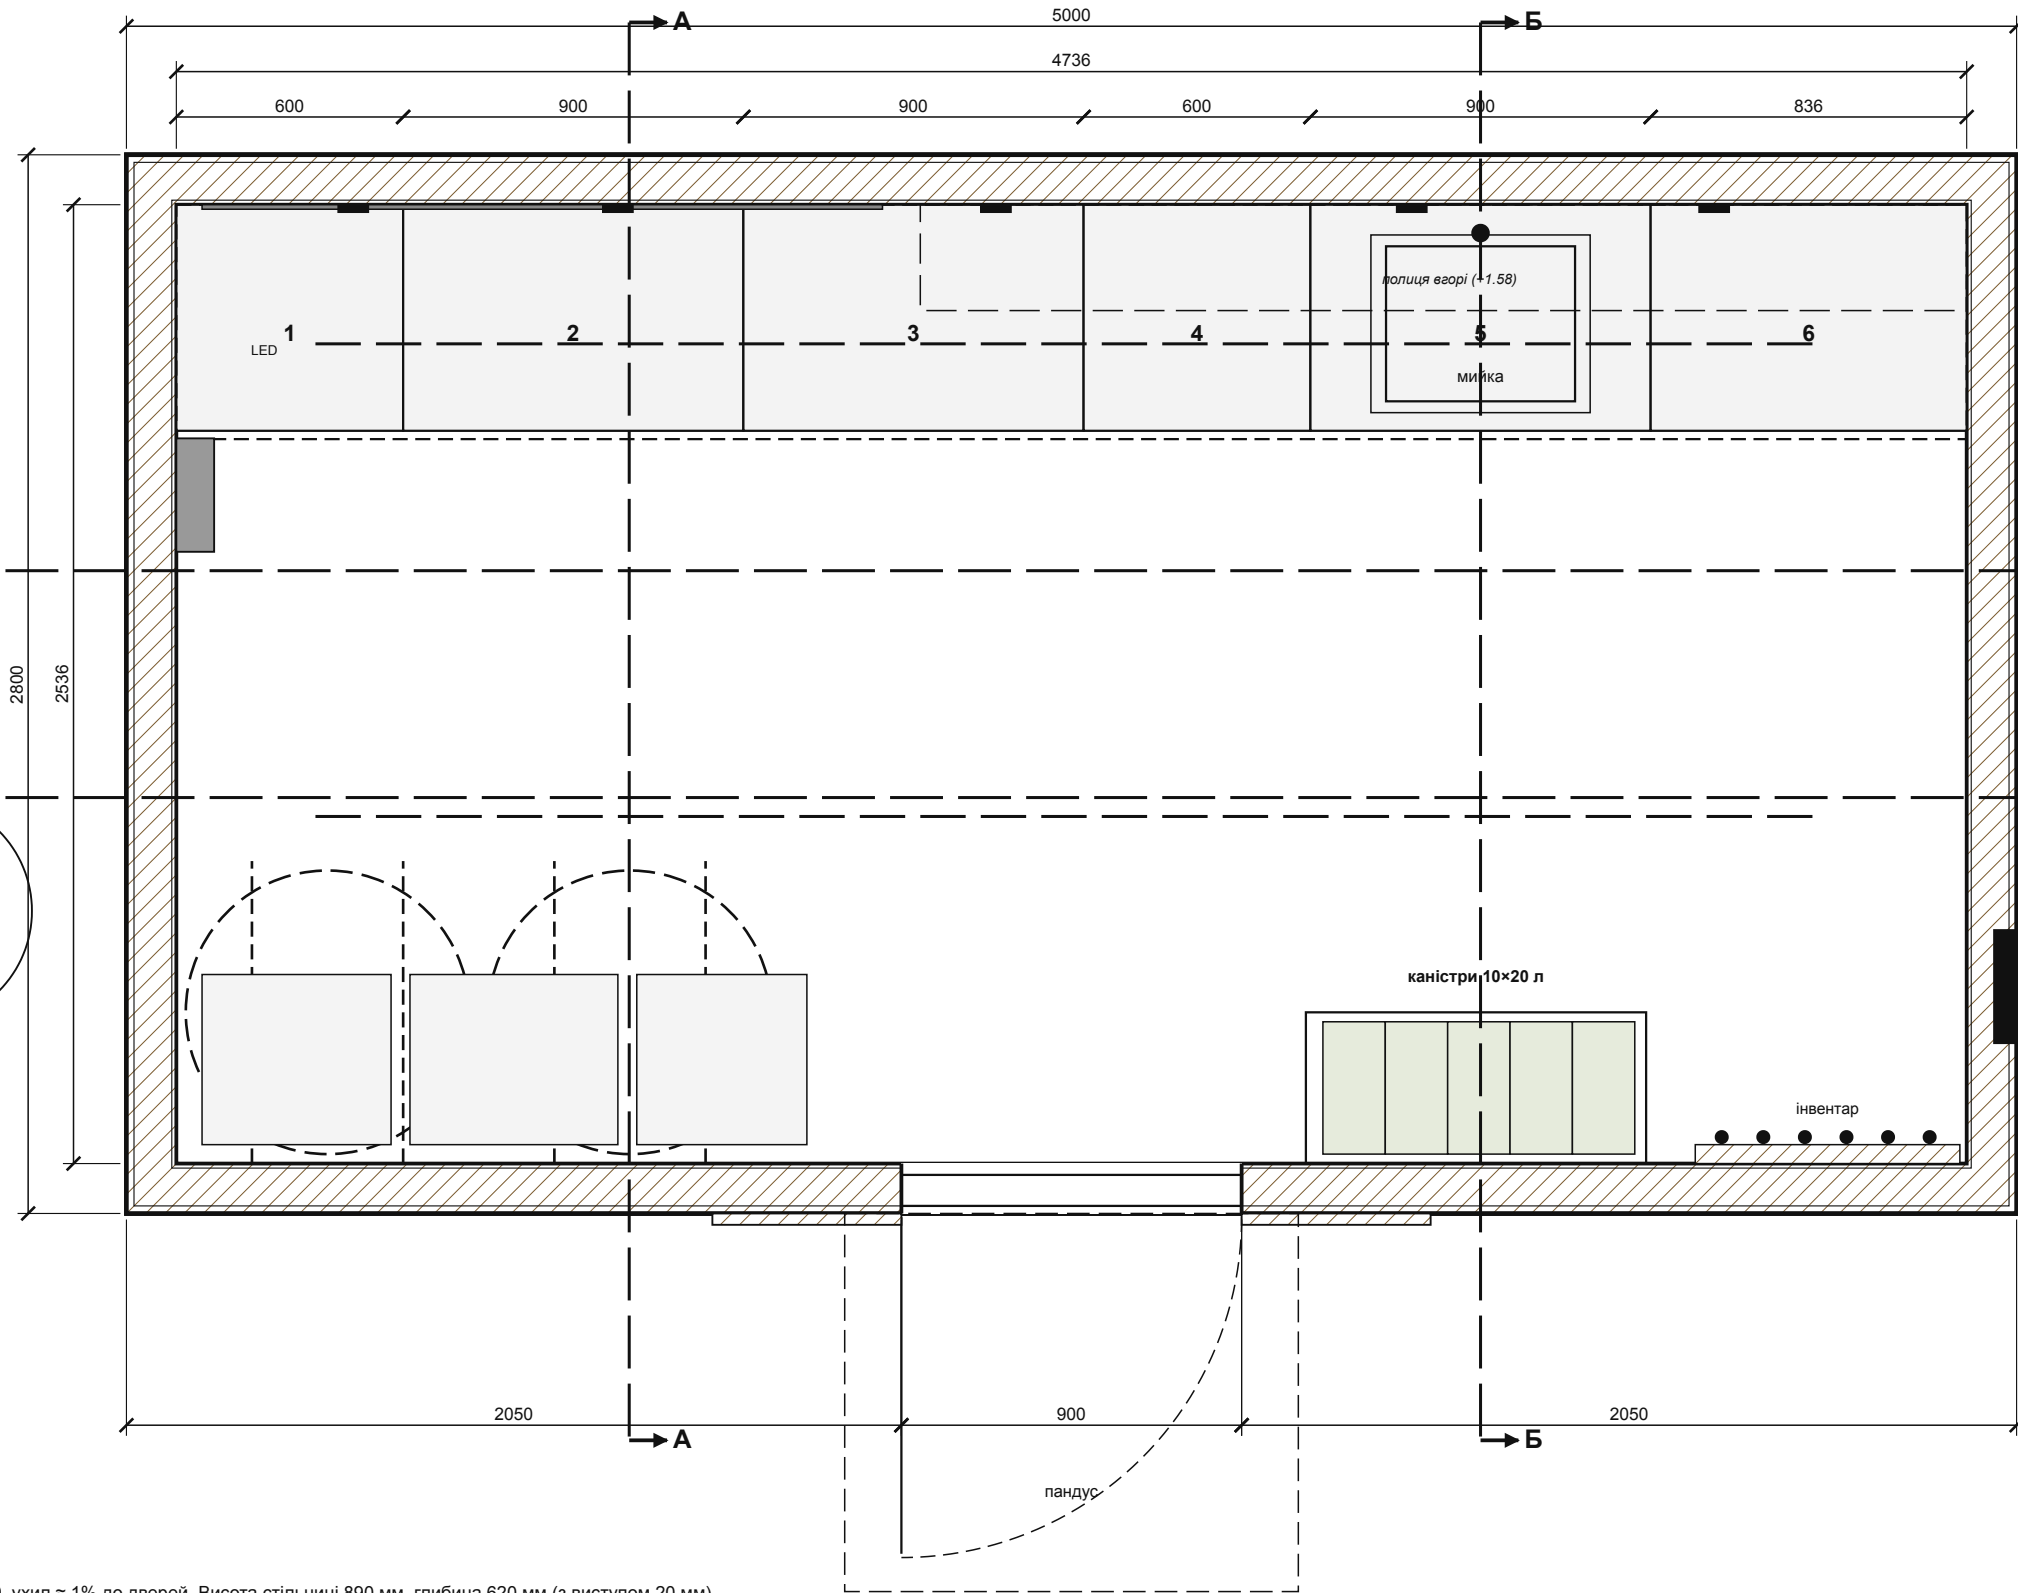

Експлікація

- 1–4, 6 Шафи з ящиками (див. арк. 7)
- 5 Шафа під мийку
- Стільниця з ясена 40 мм, h = 890
- Полиця вгорі, перфопанель, LED
- Колеса R21: 2 комплекти на кронштейнах під стелею (арк. 5, 6)
- Стелаж каністр 900 × 400, 2 яруси
- Рейка інвентарю, 700 мм
- Ящики під колесами, вільна зона
- Щиток і розетки (ліва стіна)
- Решітки вентиляції (права стіна)

Бруківка 200×100×60, ухил ≈ 1% до дверей. Висота стільниці 890 мм, глибина 620 мм (з виступом 20 мм).
Колеса: 2 стопки по 4 шт., низ колеса на +1.60 від підлоги. Каністри: 2 яруси по 5, стоять вертикально.
Електрика і вода (кесон) зліва, септик праворуч. Вентиляційні решітки на правій стіні: внизу (+0.30) і вгорі (+2.45).
Проходи: від шаф до стелажа каністр 1516 мм, на рівні коліс 1116 мм.

Проект

Майстерня 5000 × 2800, Київ

Назва аркуша

План на відм. ±0.000. Розстановка


Ескізний проект · Дата 10.2026 · ±0.000 = рівень чистої підлоги

Масштаб


1:20

Аркуш


3 / 11

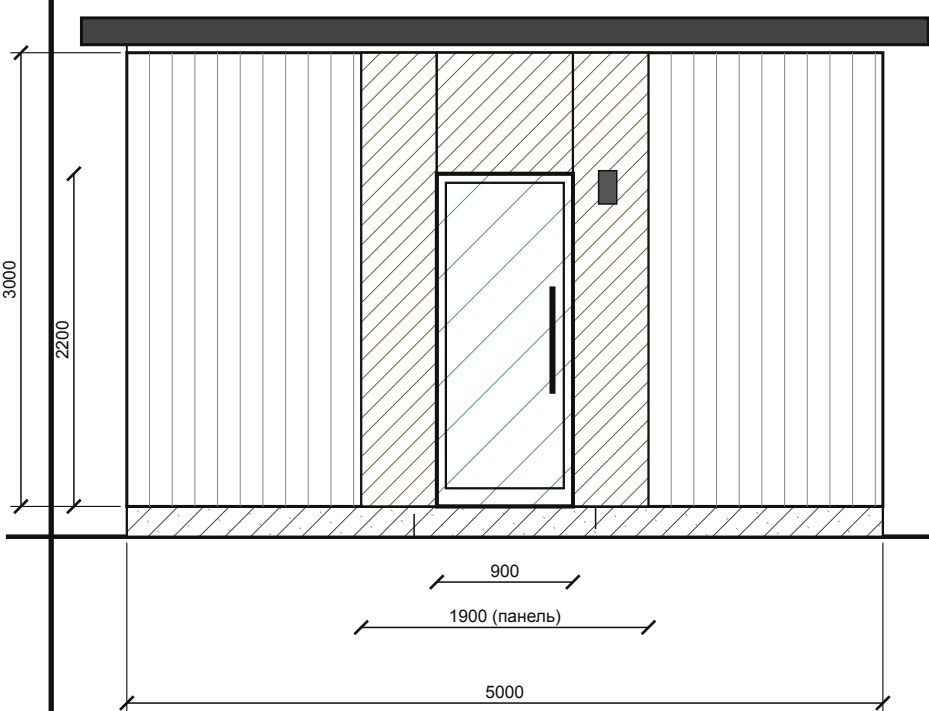


Фасад 1–5 (південний, вхід)

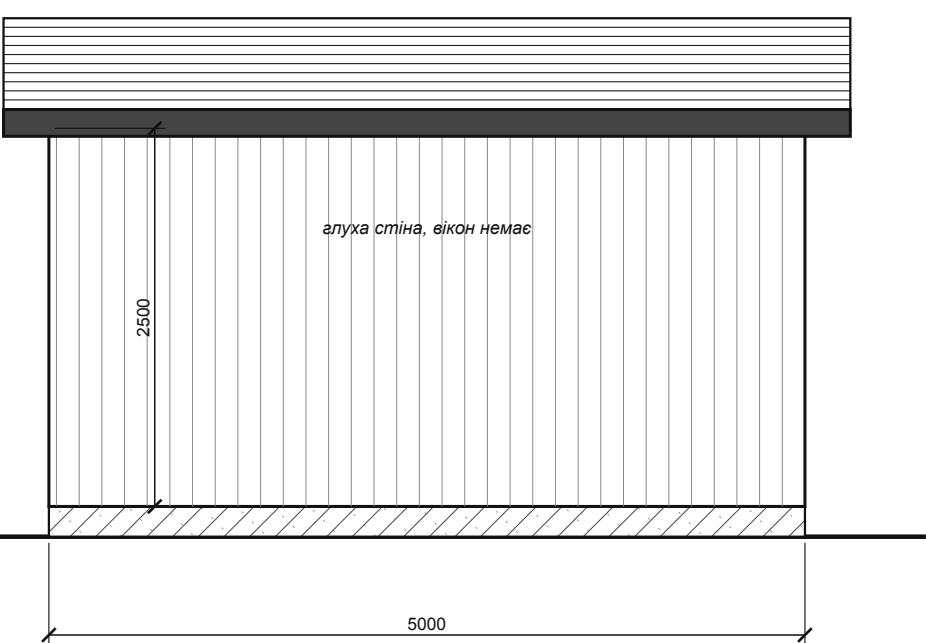

Фасад 5–1 (північний)

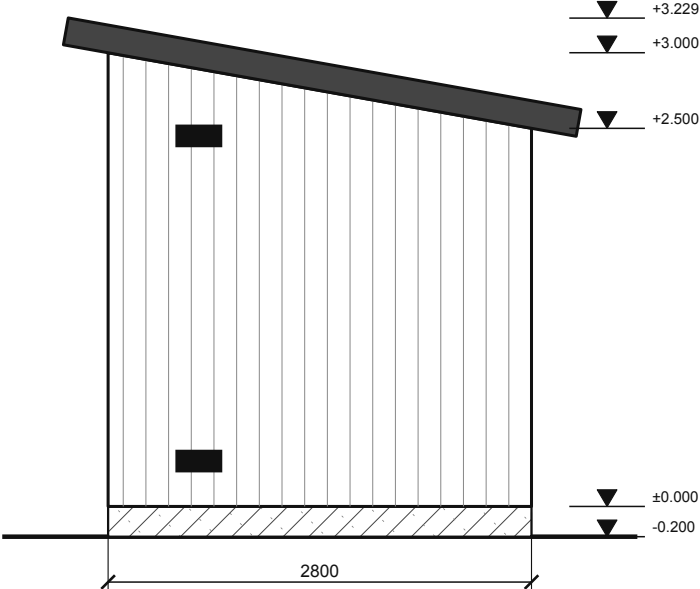

Фасад А–Г (східний)

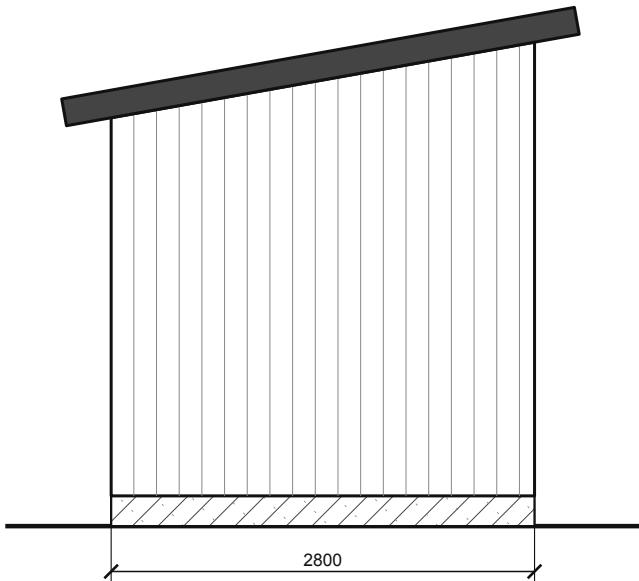

Фасад Г–А (західний)

Оздоблення

Стіни: вертикальна дошка 20 мм (дошка і рейка), білий / світло-сірий (RAL 9003 / 7035).
Панель біля дверей: модрина, вертикальні планки, масло.
Двері: алюміній, скло по всій площі, графіт (RAL 7016).
Покрівля: бітумна черепиця графіт по OSB 18, лобова дошка графіт.
Цоколь: бетон +200 над землею, пандус і доріжка з бруківки.
Решітки вентиляції 300 × 140 на східній стіні, ближче до стелажа з паливом.
Позначки рівнів у метрах від ±0.000 (чиста підлога).

Проект

Майстерня 5000 × 2800, Київ

Назва аркуша

Фасади

Ескізний проєкт · Дата 10.2026 · ±0.000 = рівень чистої підлоги


Масштаб

1:50


Аркуш

4 / 11

А–А (по колесах і шафі 2)

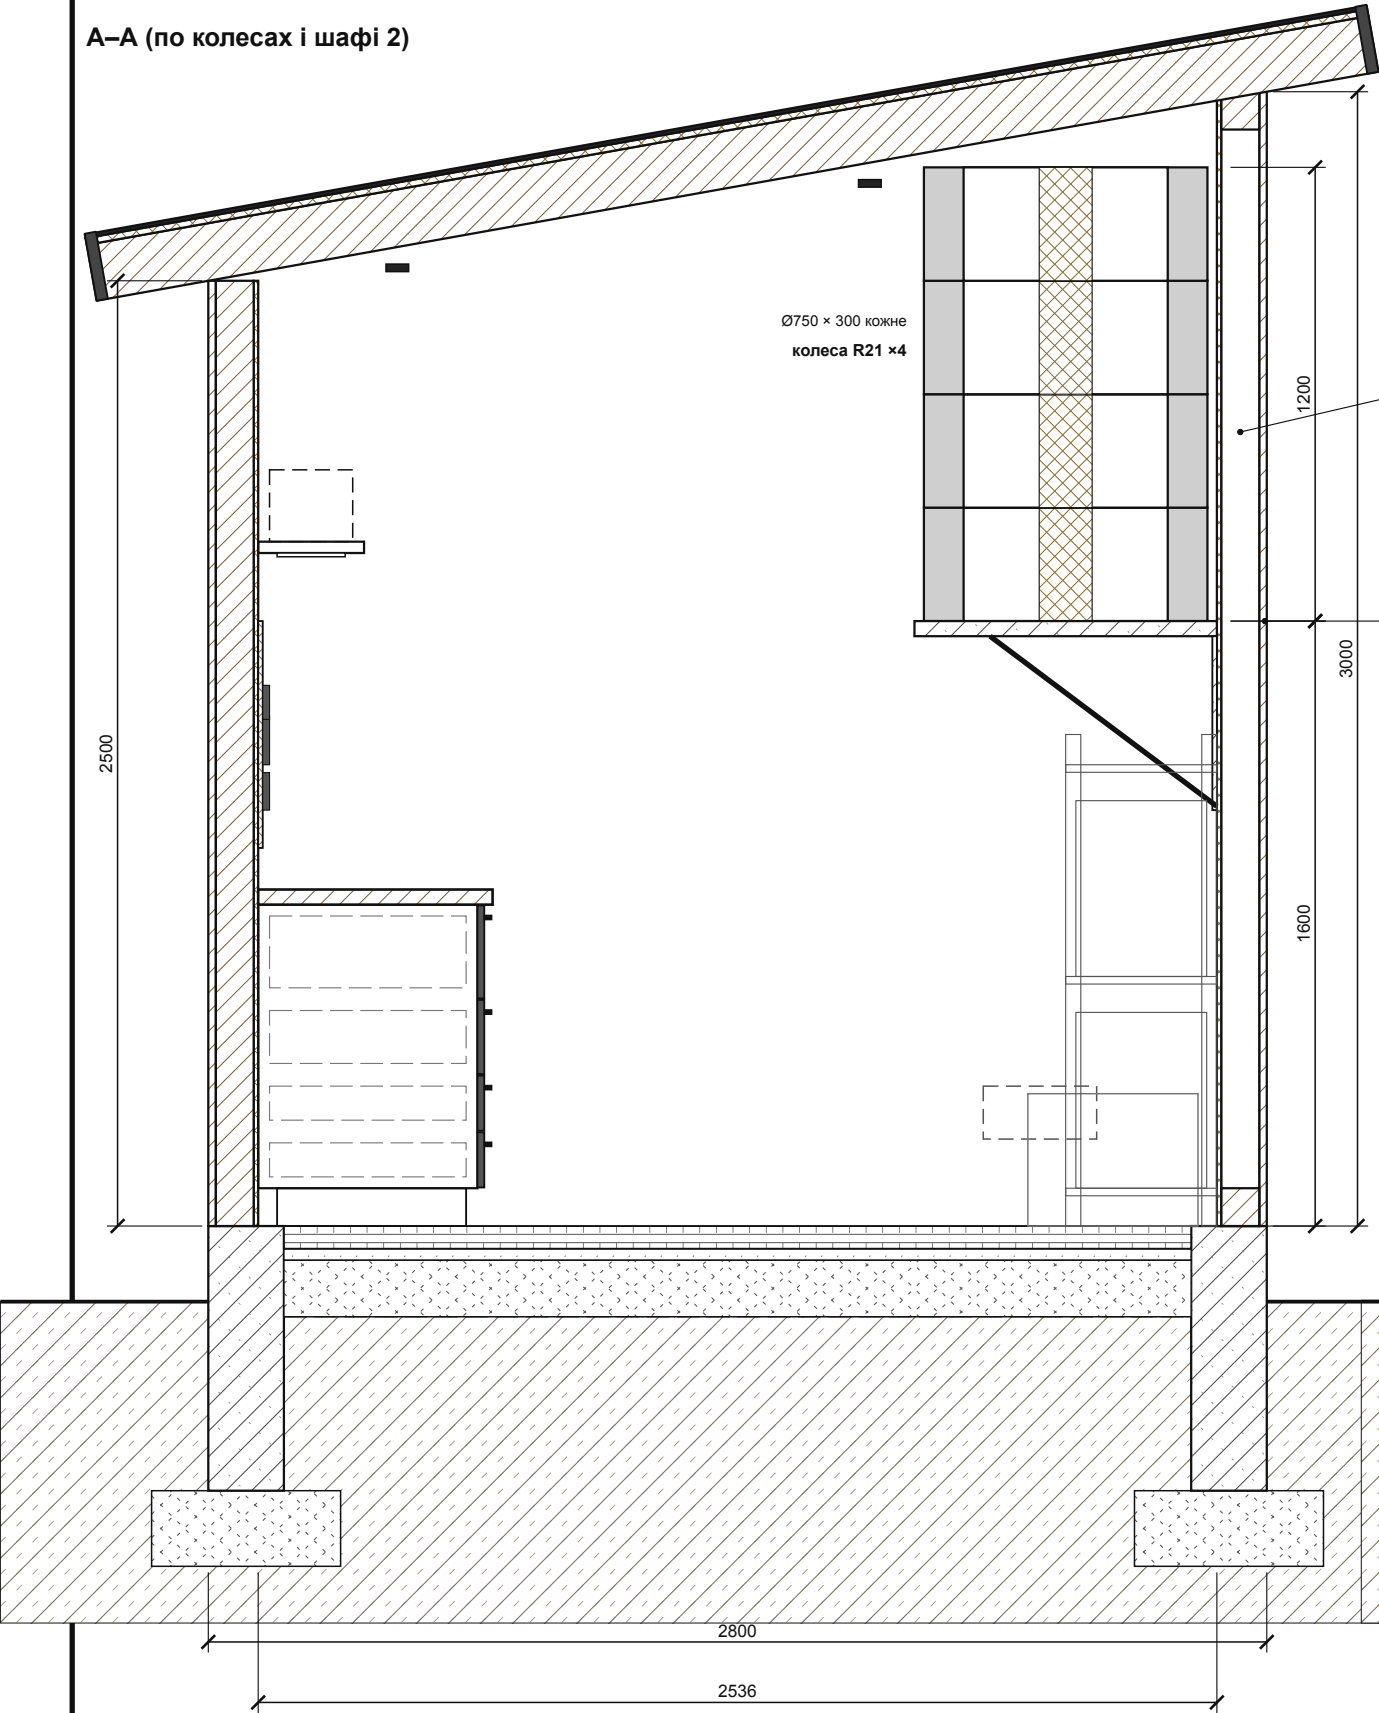

Б–Б (по мийці й каністрах)

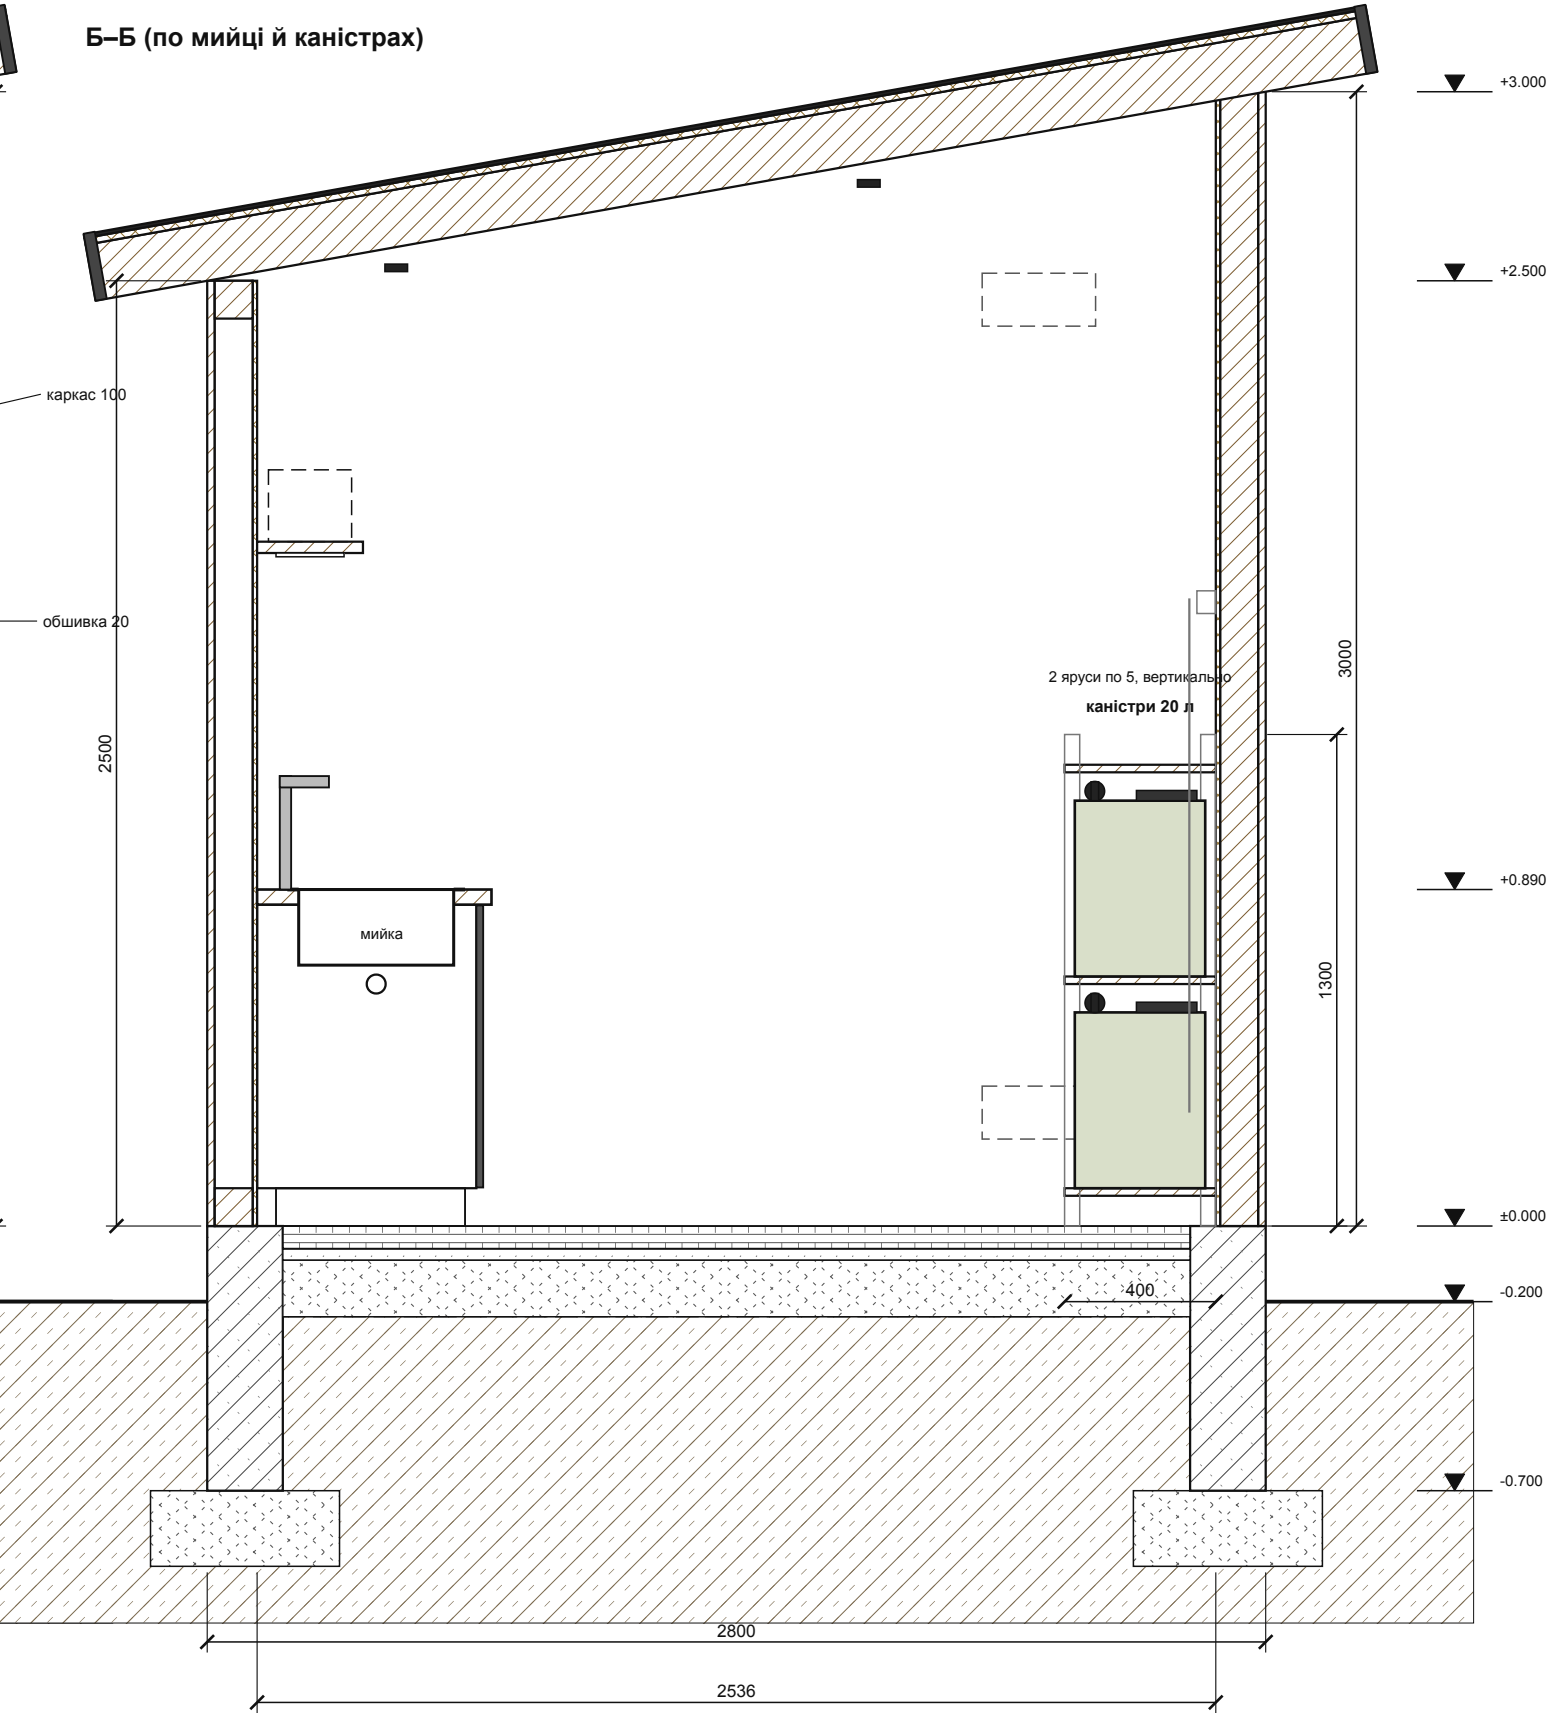

Дах: бітумна черепиця, OSB-3 18, крокви 50×150 (крок ≈ 544), нахил 10,1°.
Стіна: дошка 20, мембрана, каркас 100×100, OSB-3 12. Підлога: бруківка 60, пісок 30, щебінь 150.

Проект
Майстерня 5000 × 2800, Київ


Назва аркуша
Розрізи А–А, Б–Б

Ескізний проєкт · Дата 10.2026 · ±0.000 = рівень чистої підлоги


Масштаб
1:20

Аркуш
5 / 11

В–В (задня стіна, шафи)

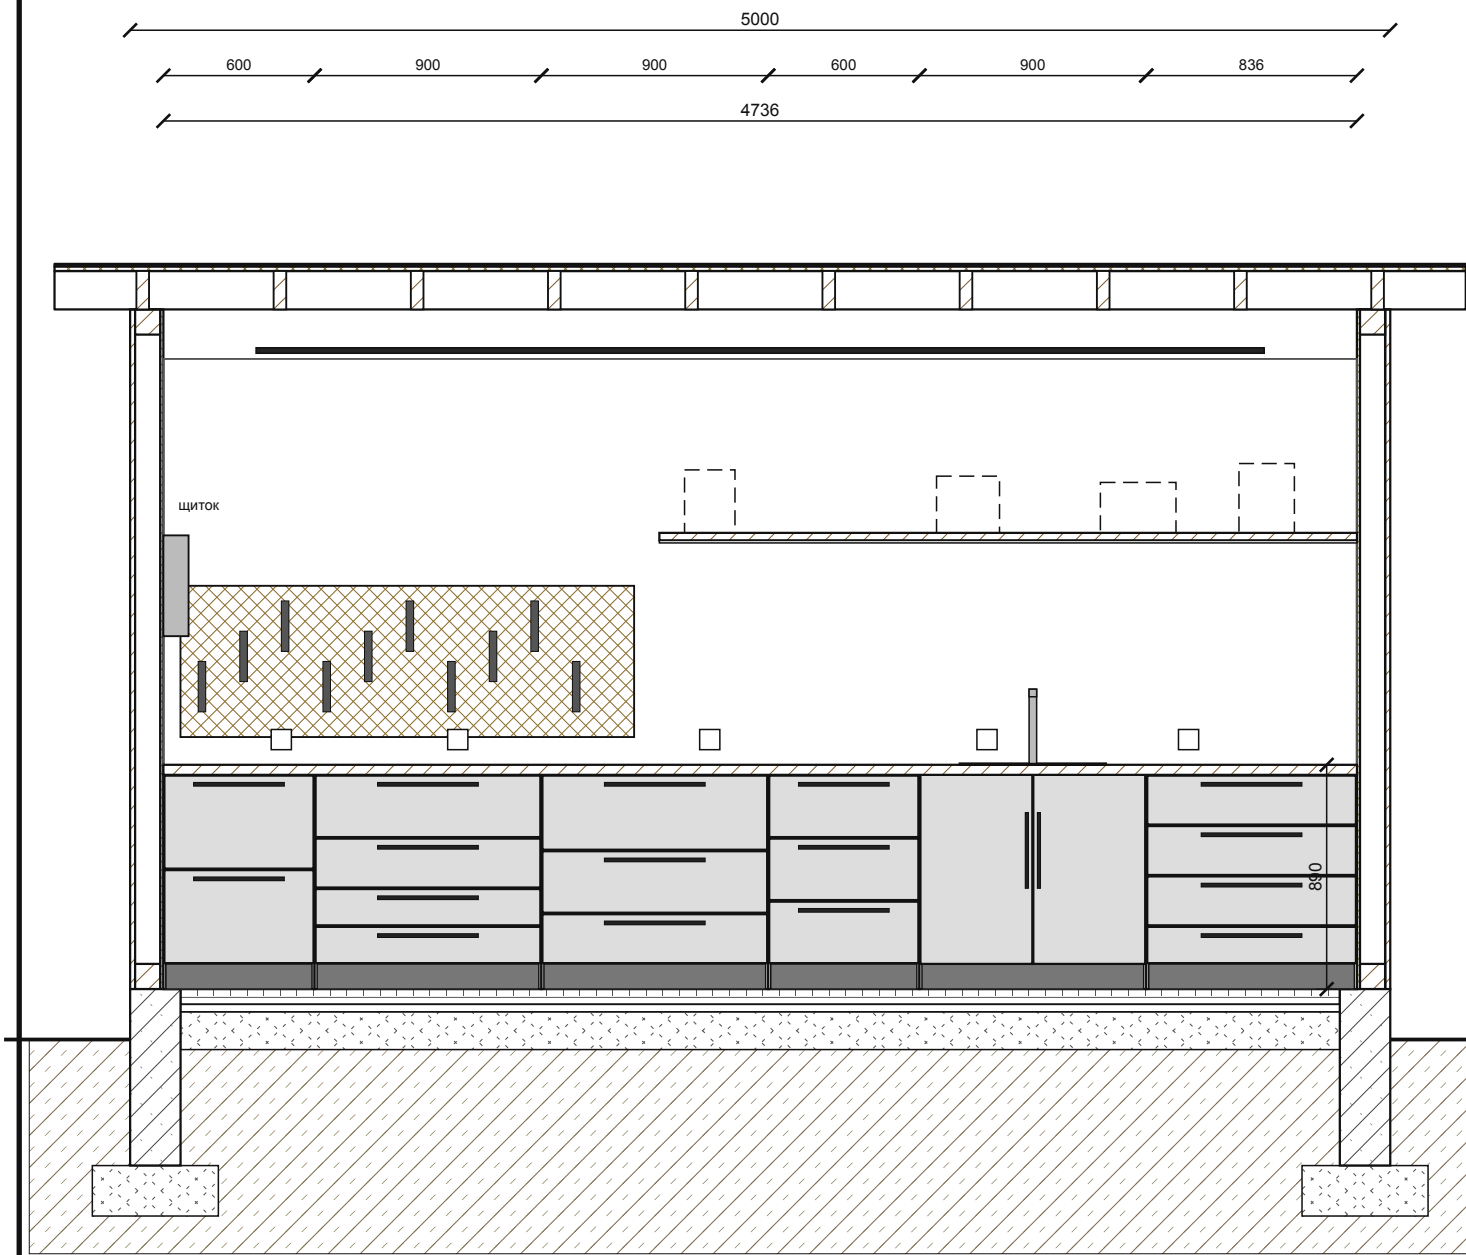

Г–Г (передня стіна, вхід)

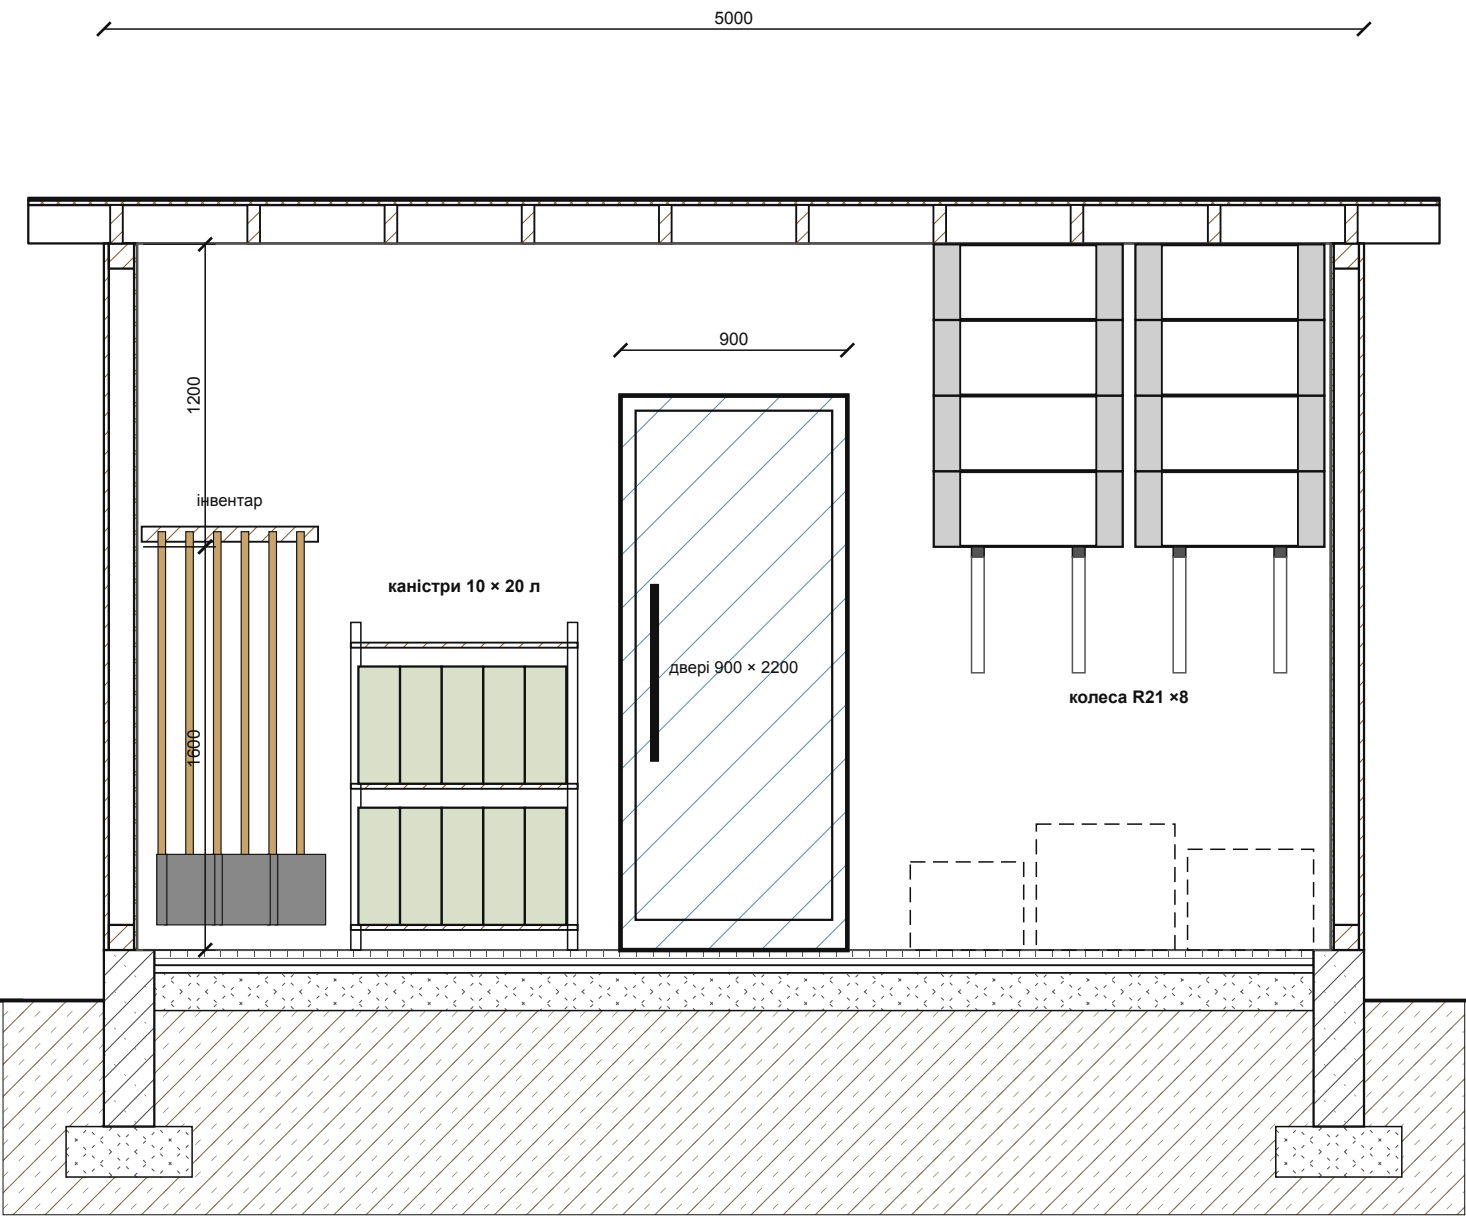



Проект
Майстерня 5000 × 2800, Київ

Назва аркуша
Розрізи В–В, Г–Г


Ескізний проєкт · Дата 10.2026 · ±0.000 = рівень чистої підлоги

Масштаб
1:30

Аркуш
6 / 11

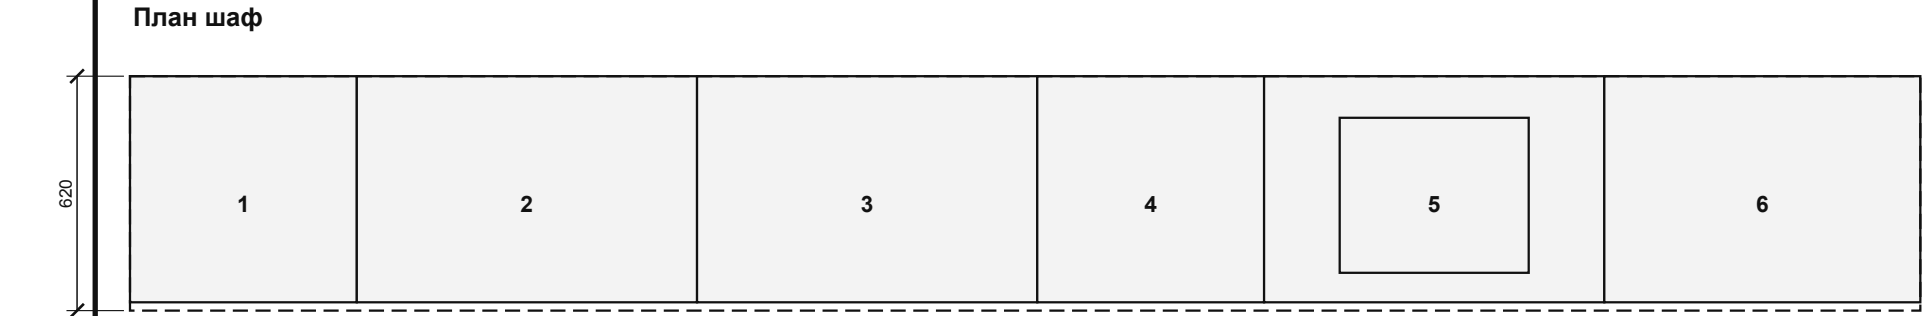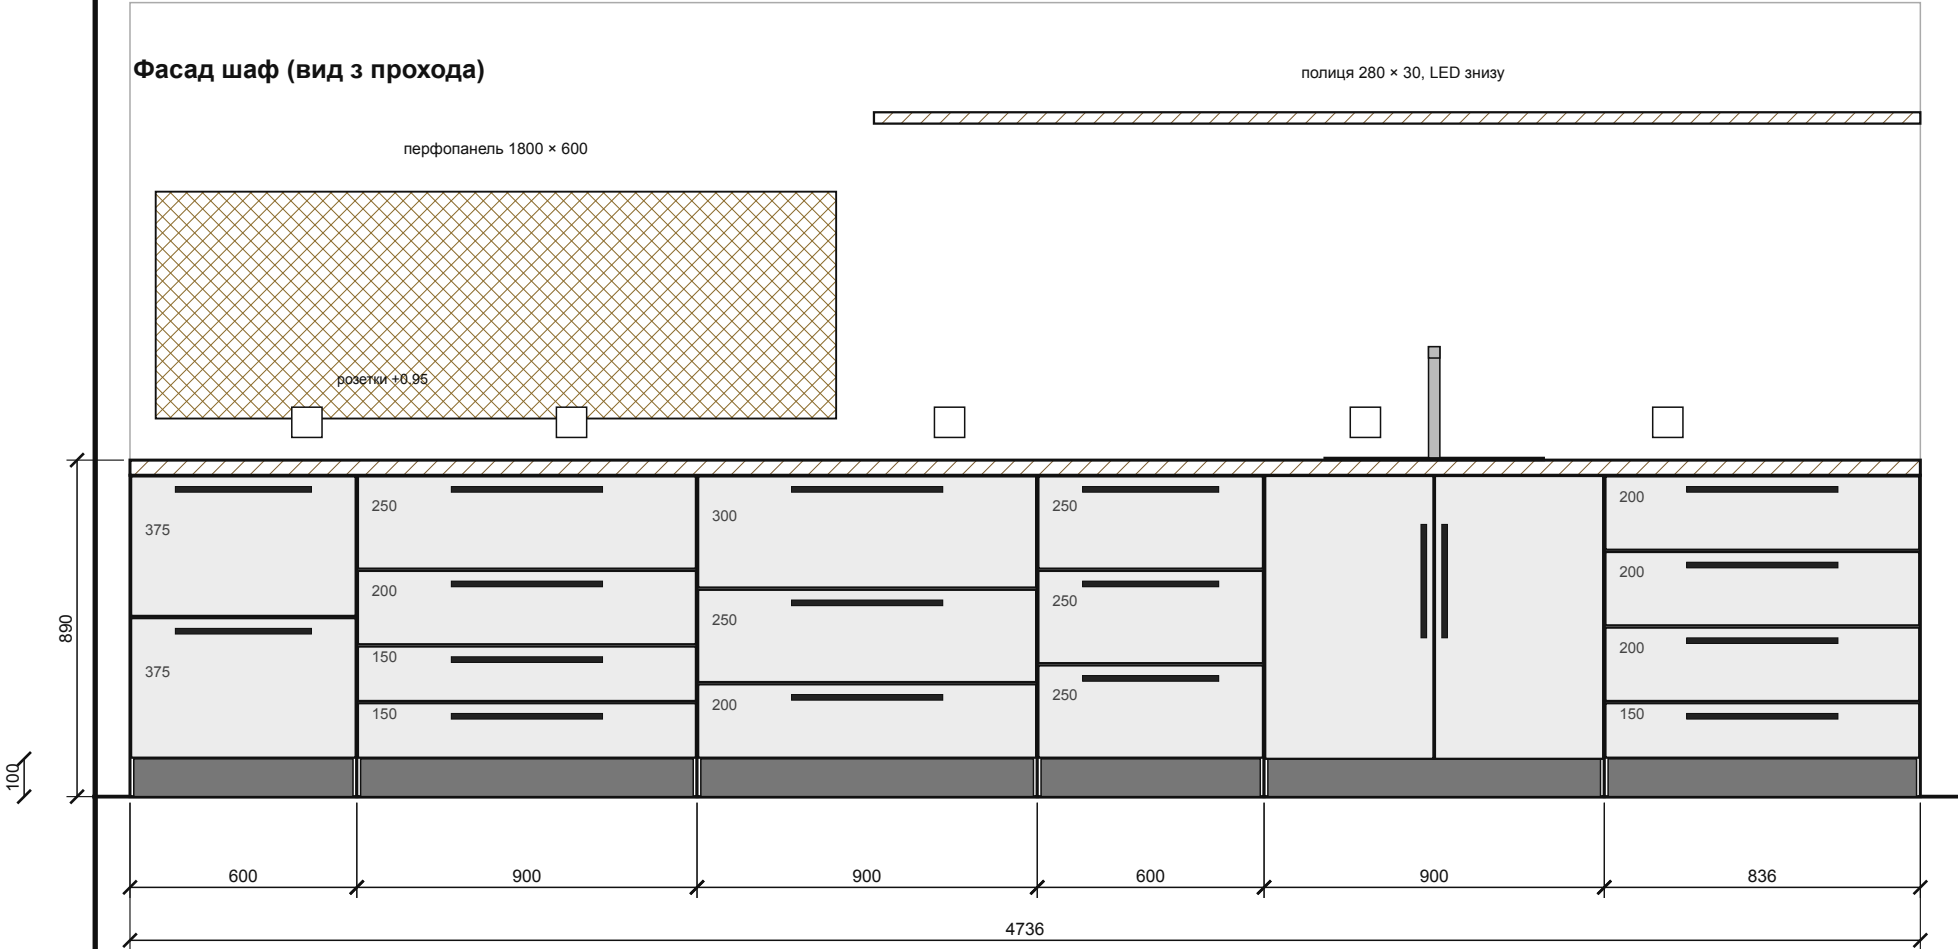

Переріз шафи №2, 1:10

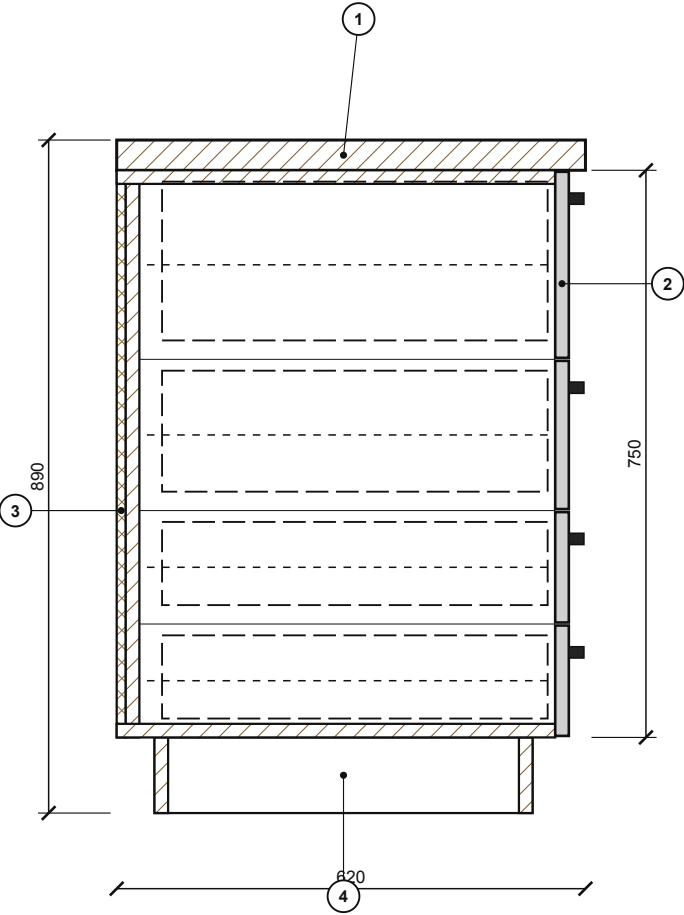

- 1 Стільниця: ясен 40, масло з воском
2 Фасад ящика: фанера/МДФ 18, графіт
3 Задня стінка: OSB/фанера 12
4 Цоколь 100, відступ 50 від фасаду

Склад шаф

№1 (600): 2 глибокі ящики по 375 мм: кейси, ударний інструмент
№2 (900): 4 ящики 150 / 150 / 200 / 250 мм: ручний інструмент
№3 (900): 3 глибокі ящики 200 / 250 / 300 мм: садовий і побутовий
№4 (600): 3 ящики по 250 мм: кріплення, витратники
№5 (900): мийка, 2 дверцят, сифон, відро. №6 (836): 4 ящики 150 / 200 / 200 / 200 мм: електрика, сантехніка

Корпус: береза/вологостійка фанера 18. Направляючі повного висування, навантаження 45 кг (16 пар).
Ширини модулів дають 4736 мм: 600 + 900 + 900 + 600 + 900 + 836.

Проект
Майстерня 5000 × 2800, Київ


Назва аркуша
Робоча поверхня і шафи

Ескізний проєкт · Дата 10.2026 · ±0.000 = рівень чистої підлоги


Масштаб
1:20 · 1:10

Аркуш
7 / 11


Каркас південної стіни, М 1:30

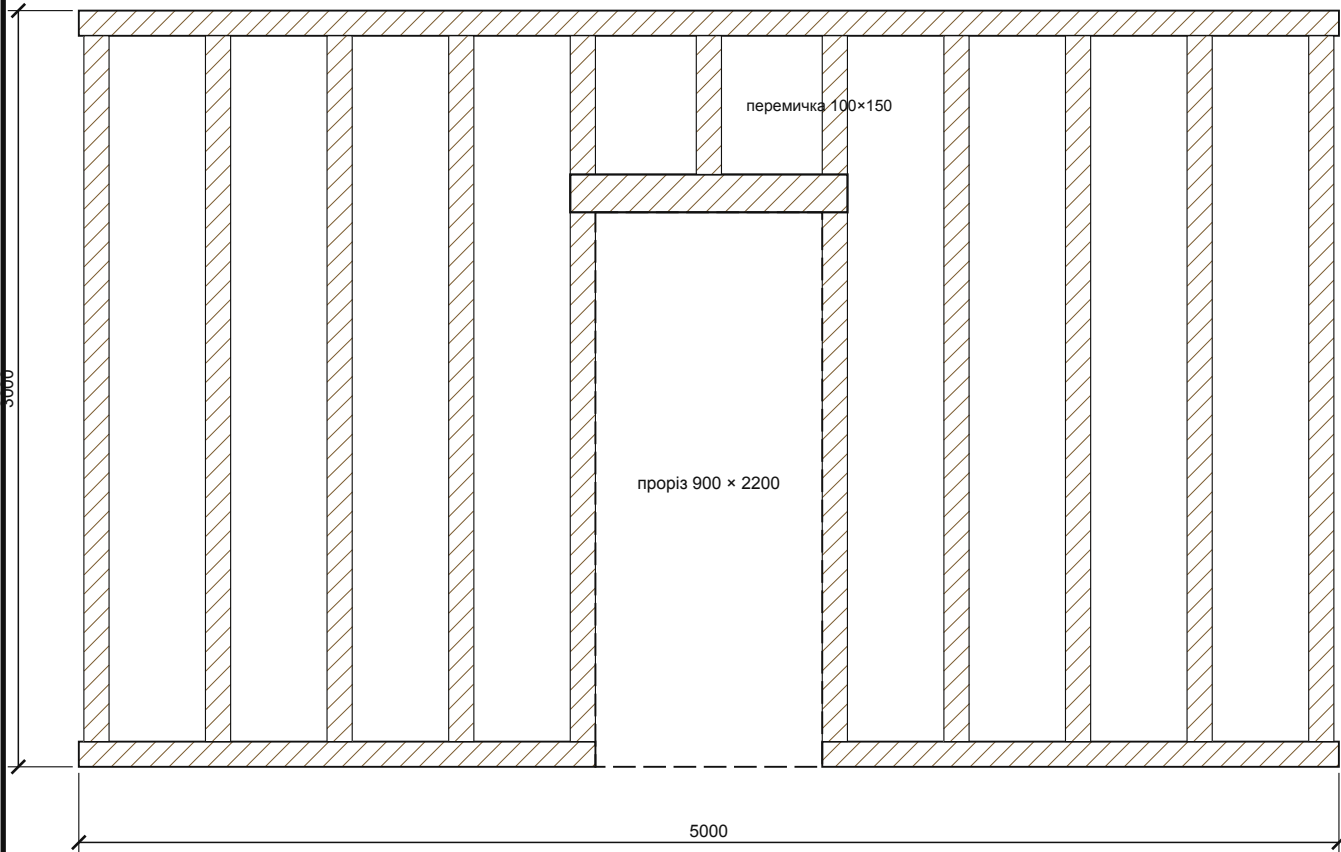


Каркас північної стіни, М 1:30

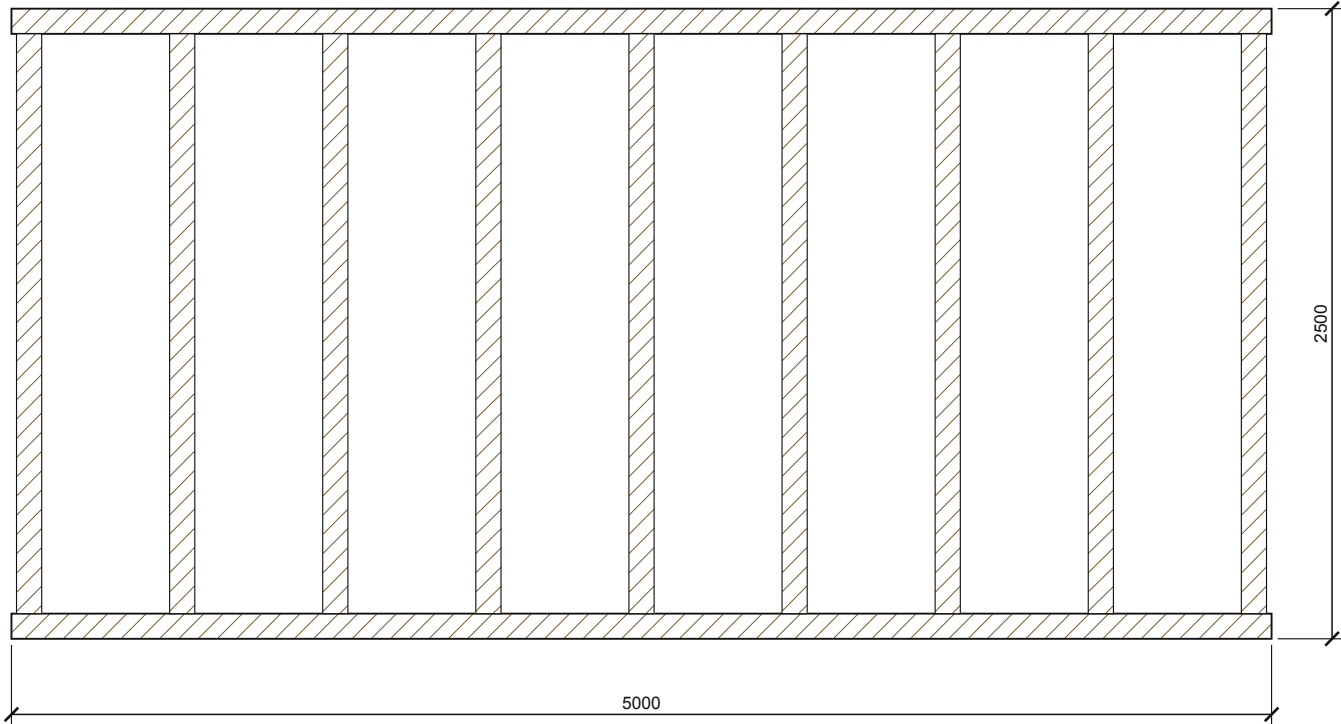

План крокв, М 1:50

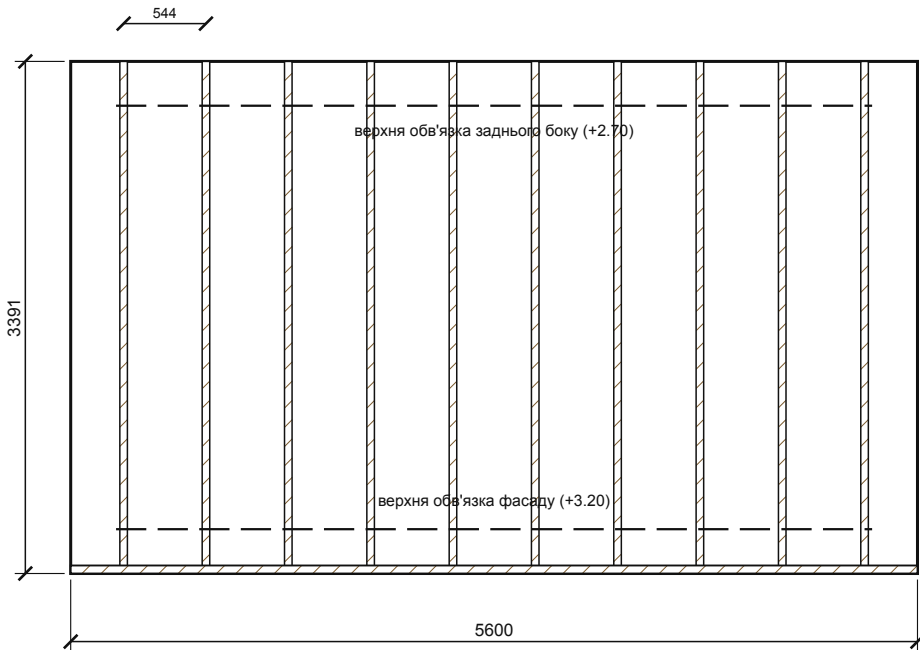

Бічна стіна (× 2), М 1:30

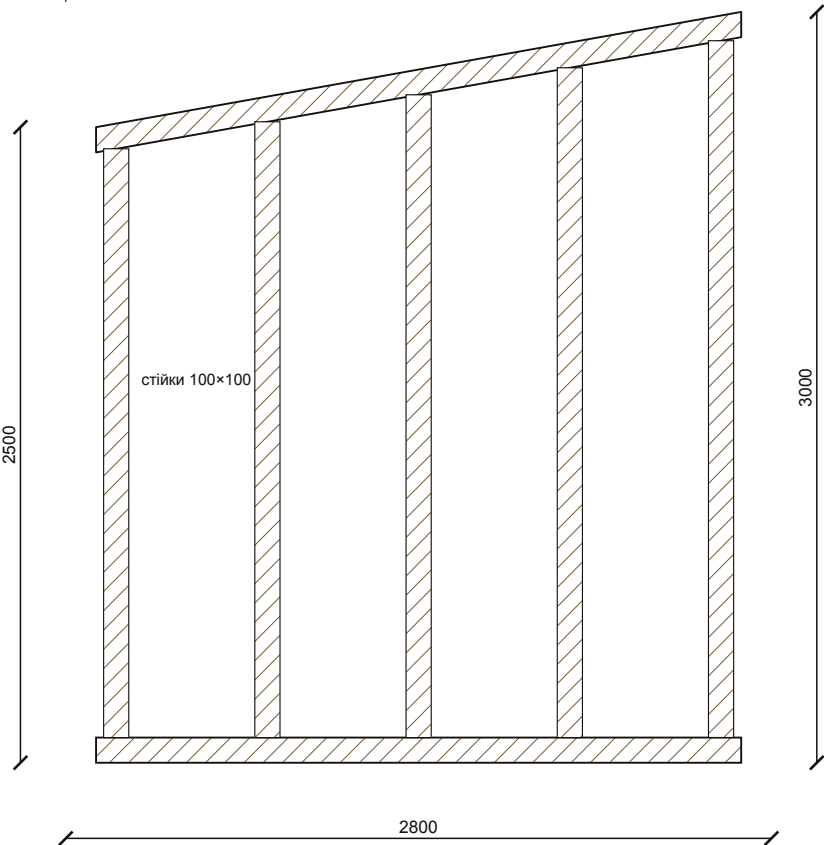

Сійки 100×100 по периметру, крок ≈ 600 мм.
Обв'язка 100×100 внизу й угорі, кути на пластинах.
Перемичка над дверима 100×150.

Крокви 50×150, 10 шт., крок ≈ 544, довжина 3444.
Нахил 10,1°, посадка на обв'язку з вирізом ≈ 20.
Лобова дошка 30×180 по периметру.

Проект

Майстерня 5000 × 2800, Київ

Назва аркуша

Каркас: стіни та дах

Ескізний проєкт · Дата 10.2026 · ±0.000 = рівень чистої підлоги


Масштаб

1:30 · 1:50

Аркуш


8 / 11

Вузол 1. Цоколь, стіна, підлога

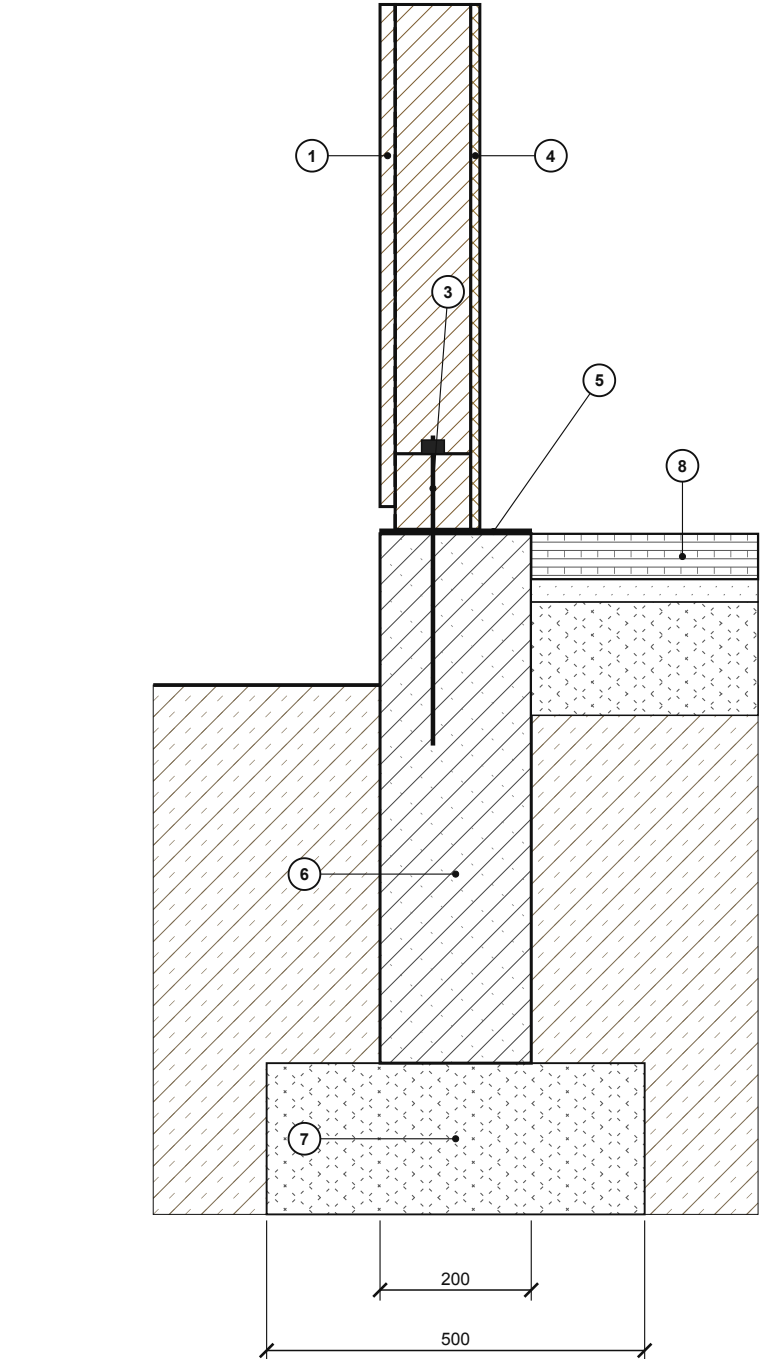


- 1 Дошка 20, низ на 30 вище цоколя
- 2 Вітрозахисна мембрана (штрих)
- 3 Нижня обв'язка 100×100, анкер M12
- 4 OSB-3 12, білий
- 5 Гідроізоляція: 2 шари руберойду
- 6 Стрічка 200×500, бетон C16/20
- 7 Щебінь 200, подушка
- 8 Підлога: бруківка 60, пісок 30, щебінь 150

Вузол 2. Карниз на фасаді (висока сторона)

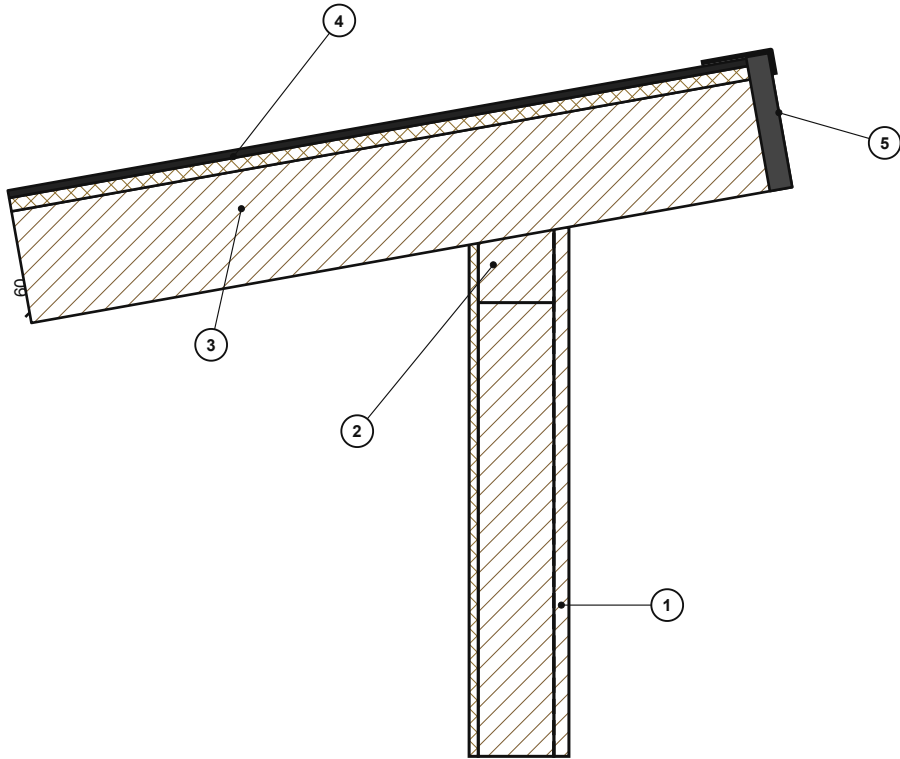

- 1 Дошка 20 + мембрана, каркас 100×100, OSB 12
- 2 Верхня обв'язка 100×100
- 3 Крокви 50×150, посадка з вирізом ≈ 20
- 4 OSB-3 18, підкладковий килим, бітумна черепиця
- 5 Лобова дошка 30×180, карнизна планка (метал)
- Виніс карниза ≈ 300 мм.

Вузол 3. Карниз на задній стіні (низька сторона)

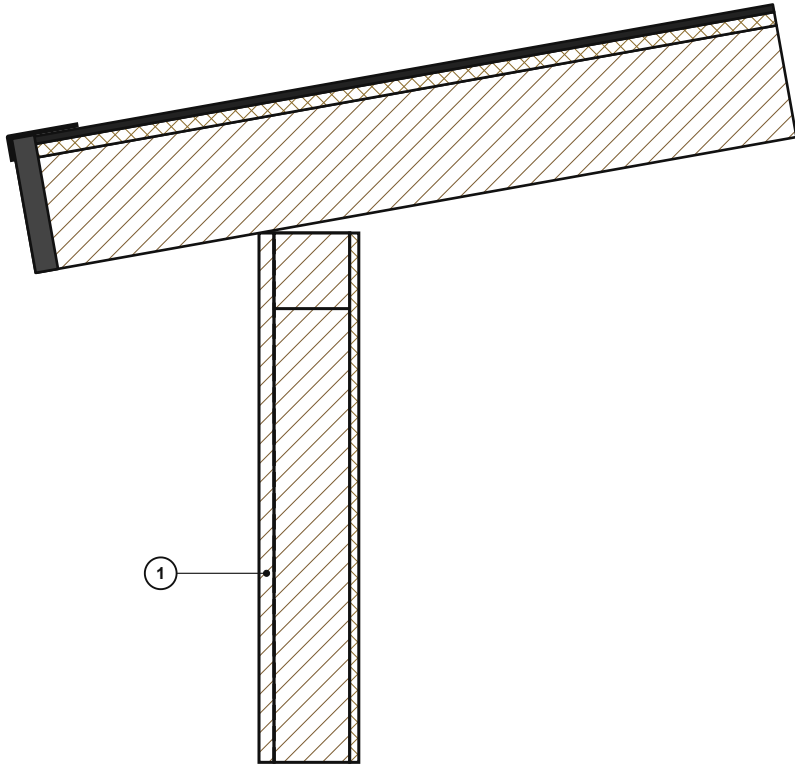

- Задня стіна: ті ж шари, висота 2500 над підлогою.
- Стікання води на задній бік від фасаду.
- Жолоб і труба на вибір замовника (напрямок до кесона або дренажу).

Проект
Майстерня 5000 × 2800, Київ


Назва аркуша
Вузли 1–3: цоколь, карнизи

Ескізний проект · Дата 10.2026 · ±0.000 = рівень чистої підлоги

Масштаб
1:10


Аркуш
9 / 11

Вузол 4. Кут (план), М 1:5

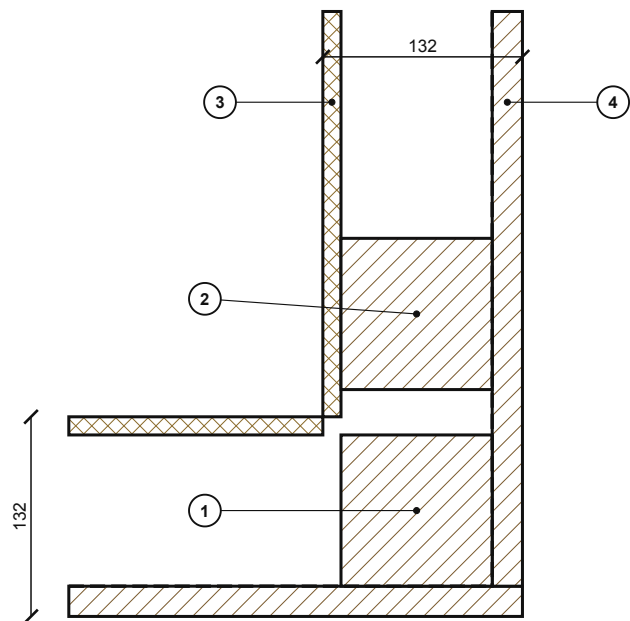

- 1 Кутова стійка 100×100
2 Сійка бійної стіни 100×100
3 OSB-3 12 всередині
4 Дошка 20 + мембрана, кут закрито двома дошками


Вузол 5. Поріг і пандус, М 1:10

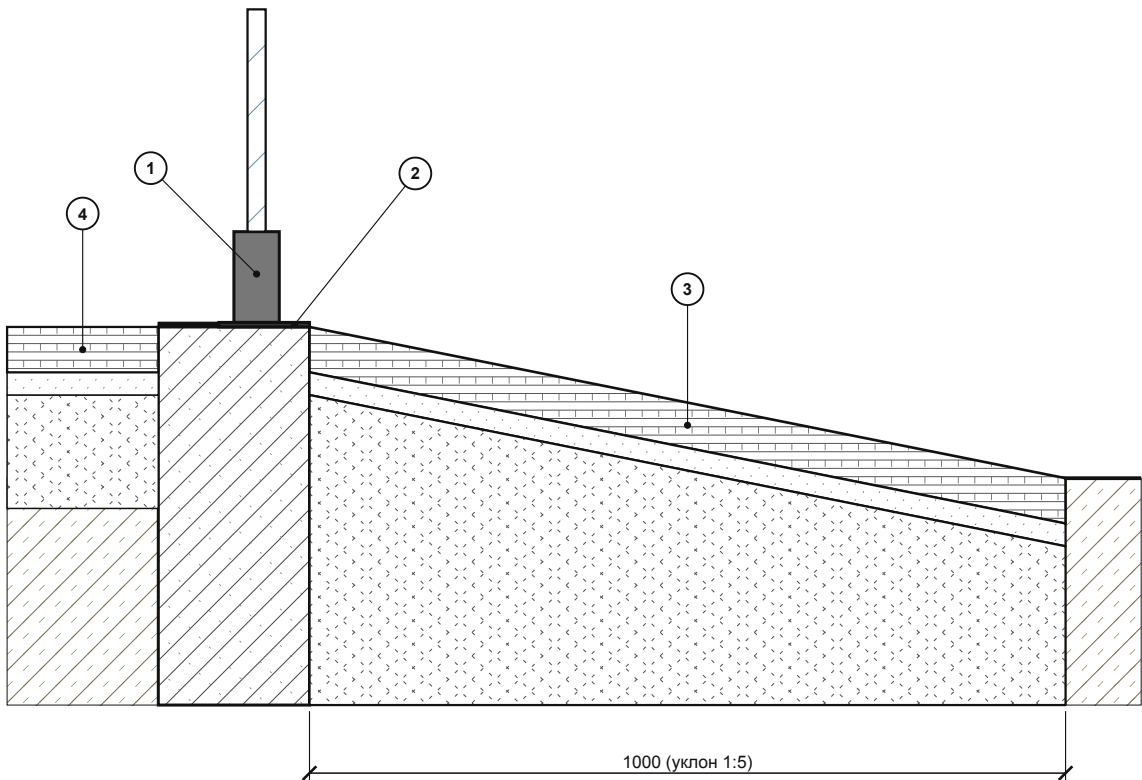

- 1 Нижня планка дверей, алюміній 60×120
2 Поріг: алюмінієвий профіль на гідроізоляції
3 Бруківка 60, пісок 30, щебінь на пандусі
4 Підлога: бруківка 60, пісок 30, щебінь 150
Пандус 1:5 крутий для візка. Бажано подовжити до 1600–2000 мм (1:8...1:10).


Вузол 6. Склад шарів, М 1:4

Стіна (ззовні всередину)

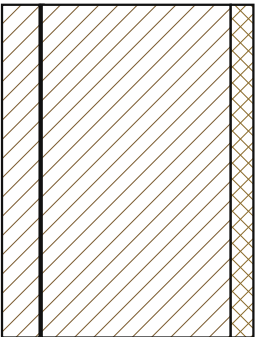


- 20 дошка (дошка й рейка)
мембрана
100 каркас, без утеплення
12 OSB-3, білий

Дах (зверху вниз)

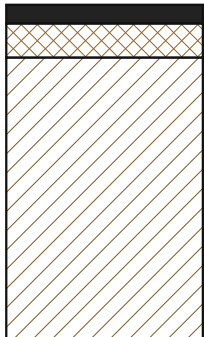

- 10 бітумна черепиця
18 OSB-3 + підкладковий килим
150 крокви 50×150

Підлога (зверху вниз)

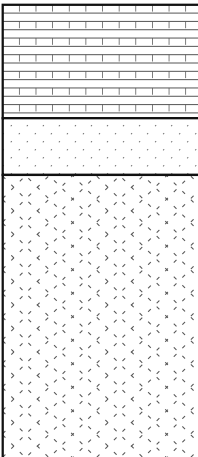

- 60 бруківка 200×100
30 пісок
150 щебінь, геотекстиль

Проект

Майстерня 5000 × 2800, Київ

Назва аркуша

Вузли 4–6: кут, поріг, шари

Ескізний проект · Дата 10.2026 · ±0.000 = рівень чистої підлоги

Масштаб

1:5 · 1:10 · 1:4

Аркуш

10 / 11

Специфікація матеріалів (орієнтовна, з запасом ≈ 10%)

Позиція	Од.	К-сть	Примітка
Фундамент			
Бетон C16/20 (стрічка)	м³	2,1	≈ 14,8 м × 0,2 × 0,7
Арматура Ø12 A500C	м	60	4 нитки по периметру
Арматура Ø6 (хомути, крок 400)	м	55	
Опалубка: дошка 25×150	м	50	над землею 200 мм
Щебінь 20–40	м³	3,6	подушка стрічки 1,5 + підлога 1,7
Пісок	м³	0,8	під бруківку, пандус, доріжку
Геотекстиль	м²	15	
Руберойд (гідроізоляція стрічки)	м²	8	2 шари
Анкери M12×200	шт	20	
Бруківка 200×100×60	шт	900	підлога 12 м² + пандус і доріжка 4,3 м²
Каркас і стіни			
Брус 100×100 (стійки, обв'язка)	м	117	≈ 20 шт по 6 м
Брус 100×150 (перемичка дверей)	м	1,2	
Дошка 50×150 (крокви)	м	48	10 шт × 3,5 м + запас
Вітрозахисна мембрана	м²	50	1 рулон 75 м²
Дошка обшивки 20 (дошка і рейка)	м²	46	біла фарба / лазур
Модрина, планки 20 (панель дверей)	м²	4	
OSB-3 12 мм, 2500×1250 (внутрішня обшивка)	арк	14	≈ 39 м² + підрізка
Дах			
OSB-3 18 мм, 2500×1250 (настил)	арк	8	19,3 м² + запас
Підкладковий килим	м²	30	по всій площі, 2 рулони
Бітумна черепиця (уп. 3 м²)	уп	8	площа 19,3 м²
Карнизна і торцева планка (метал)	м	19	по периметру даху
Лобова дошка 30×180	м	18	
Бітумна мастика, цвяхи покрівельні	компл	1	
Меблі та обладнання			
Фанера береза 18, 1525×1525	арк	8	корпуси шаф, фасади
Щит ясеневий 40 мм (стільність)	м²	3,2	4736 × 620
Направляючі повного висування, 45 кг	пар	16	
Мийка нерж., змішувач, сифон	компл	1	
Сталевий профіль 40×40×3 (кронштейни коліс)	м	7	4 консолі + 4 розкоси, плити
Брус 40×40 і дошка 25×100 (стелаж каністр)	м	12	
LED-лінійки 4000 K, розетки, щиток	компл	1	розетки ≈ 6 шт

Кількості орієнтовні, їх треба уточнити після шурфа і остаточного вибору виробників. Ціни не наведено.
Двері (алюмінієві скляні 900 × 2200) і сантехнічні вводи наявні на об'єкті.

Проект

Майстерня 5000 × 2800, Київ

Назва аркуша

Специфікація матеріалів

Ескізний проєкт · Дата 10.2026 · ±0.000 = рівень чистої підлоги

Масштаб

—

Аркуш

11 / 11